

FALL PROTECTION PLAN

Site-Specific Work-at-Heights Safety Plan




SITE INFORMATION

Name of employer: FIREFLY SOLAR

Work site (i.e. civic address):

Period for which this plan is valid: 24 Hours

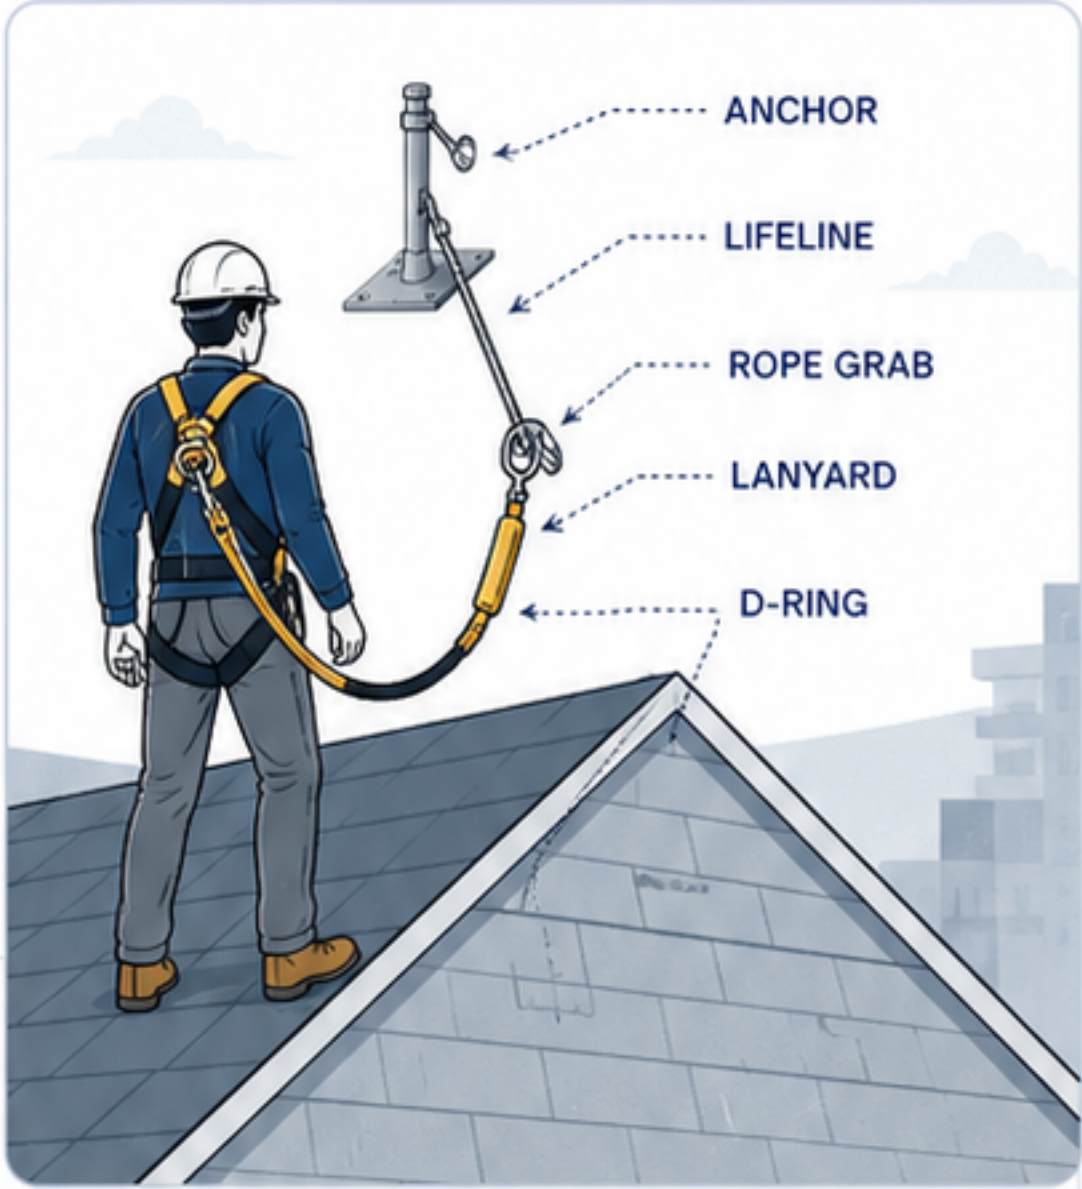

1. FALL HAZARDS AT THE WORK SITE:

Identify the specific work area and circumstances where a worker could fall (e.g. "leading edge of second floor work area", "unguarded opening on third floor", etc.)



2. FALL PROTECTION SYSTEM(S): Brief description of the system being used (fall arrest, travel restraint, fall restrict, horizontal lifeline, safety net, work positioning, control zone, etc.)

Fall Arrest System, Full Body Harness, Rope Grab, Shock Absorbing Lanyard



3. ANCHOR(S) TO BE USED: Amount and type of Anchors, permanent or reusable. Circle One:

Permanent Roof Anchors #

OR

Reusable Roof Anchors #



All anchors are to be attached to the roof structure, i.e. rafters, trusses, use a sufficient amount of screws with a minimum shear strength of 5000lbs. #10 R4 GRK screws recommended.



Harness, D-Ring, Buckles, Straps, Lanyard, Rope and Rope Grab MUST be inspected prior to each use for Rips, Tears, Fraying, Deformities, Cracks, Abnormal wear and tear, liquid contamination and deterioration. Any part of the system found to be damaged must be destroyed or sent for repair.



4. SYSTEM PROCEDURES: to assemble, maintain, inspect, use and disassemble the fall protection system:



Rope Grab must move freely up the rope and lock in the down position



Harnesses must be hung up after each use, kept clean and away from direct sun exposure while being stored



D-Ring should be in between the shoulder blades, chest strap shouldn't allow an open hand to pass through, while leg straps must not allow a closed fist to pass through



Use the buddy system to verify a coworkers harness is correctly worn



Keys, phones, tools and other items must be removed from pockets



RESCUE PROCEDURES & CLEARANCE REQUIREMENT

Emergency response, worker acknowledgement, and fall clearance calculation



1. RESCUE PROCEDURES

Select the planned method(s) for rescuing a fallen worker.

- ☐
-
- SELF RESCUE
- A worker is able to rescue themselves or pull themselves back to safety
- ☐
-
- ASSISTED ROOF RESCUE
- A worker is able to be pulled to safety by other crew members
- ☐
-
- LADDER RESCUE
- Workers on the ground position a ladder underneath the fallen worker and allow him to climb down safely
- ☐
-
- AWP RESCUE
- If a work platform is available on site and can reach the worker it is acceptable to use
- ☐
-
- FIRE DEPARTMENT RESCUE
- No viable rescue options. 911 is called and Fire Department dispatched



2. WORKER SIGN-OFF


All workers affected by this fall protection plan must review and sign.

	WORKER NAME	SIGNATURE		WORKER NAME	SIGNATURE
1.			4.		
2.			5.		
3.			6.		



3. CLEARANCE REQUIREMENT

This must be calculated (you can use the worksheet below for convenience). The distance the worker falls must be less than the distance to the ground or an object or level below the work area (such as a balcony, mezzanine, or HVAC ducting).

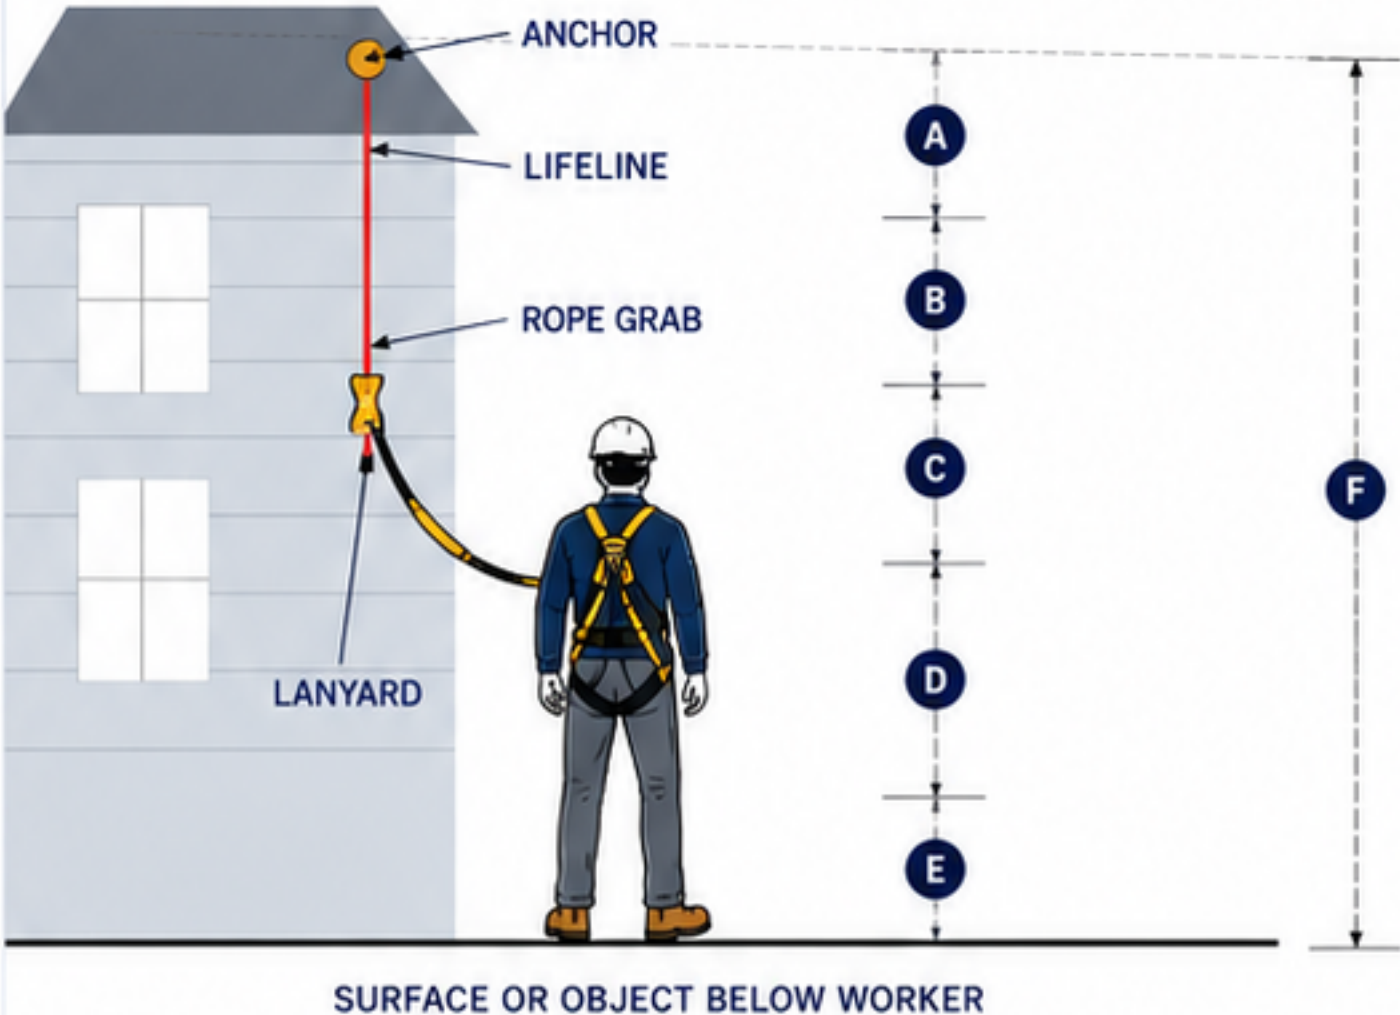

CALCULATE REQUIRED CLEARANCE

A	Distance from anchor to rope grab, plus length of lanyard	
B	Length of shock absorber extended — typically 1.1m (3.6') or 1.75m (5.7'), depending on the absorber	
C	D-ring slippage and harness stretch — 0.3m (1') minimum	
D	Height of worker's D-ring from foot level — typically 1.5m (5'), but can be longer for taller workers	
E	Safety factor — minimum 0.6m (2')	
F	SUM OF A + B + C + D + E	

i NOTE: The actual distance to the surface or object below must be greater than the clearance required. If not, a falling worker will strike that lower surface or object. A different anchor location or type of fall protection system may be required.

